




1 ALOJAMENTO – FACHADA NOROESTE
ESC.: 1:200

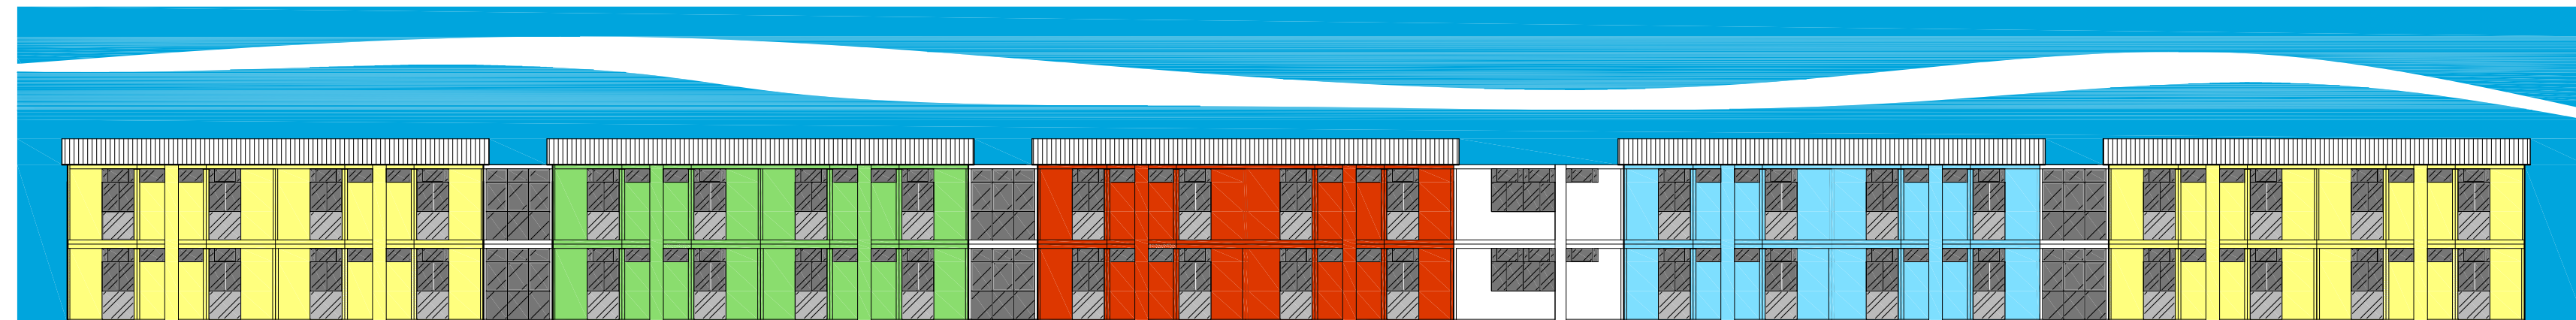


2 ALOJAMENTO – FACHADA SUDOESTE
ESC.: 1:200

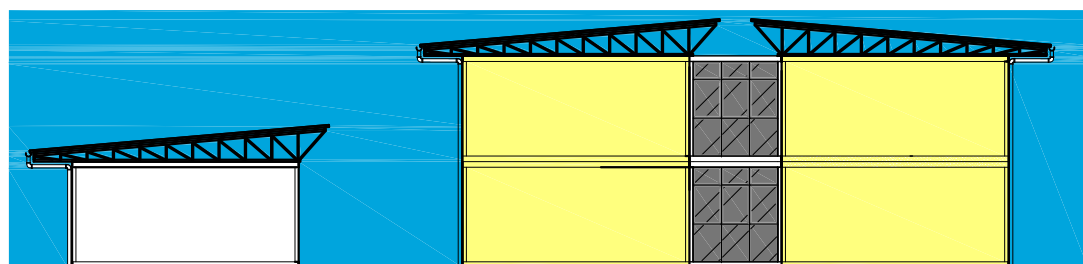


3 ALOJAMENTO – FACHADA SUDESTE
ESC.: 1:200

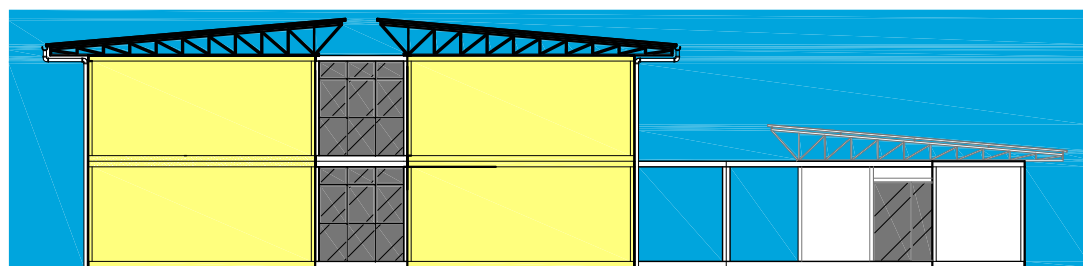


3 ALOJAMENTO – FACHADA NORDESTE
ESC.: 1:200

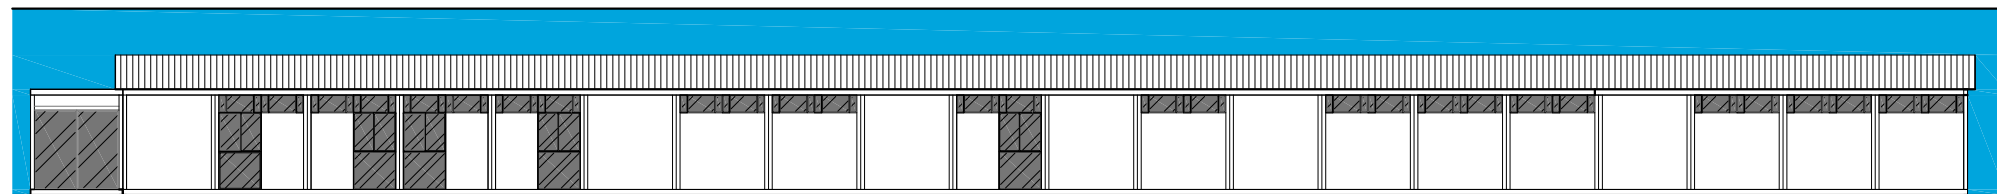


4 ÁREA DE APOIO – FACHADA NOROESTE
ESC.: 1:200

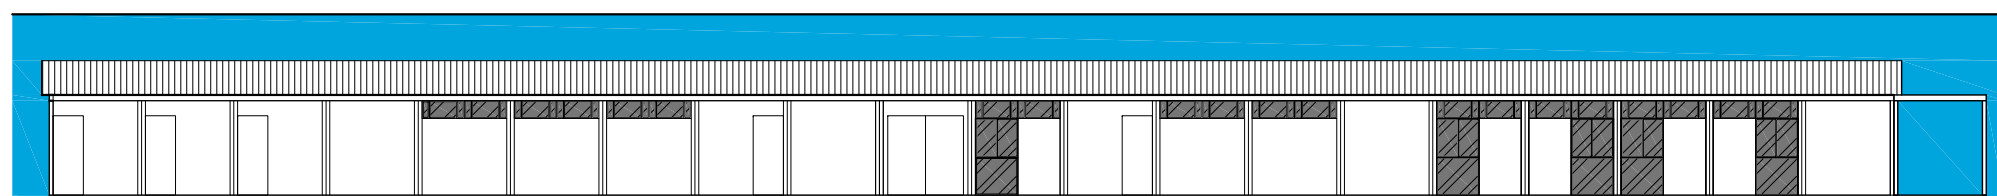


4 ÁREA DE APOIO – FACHADA SUDOESTE
ESC.: 1:200

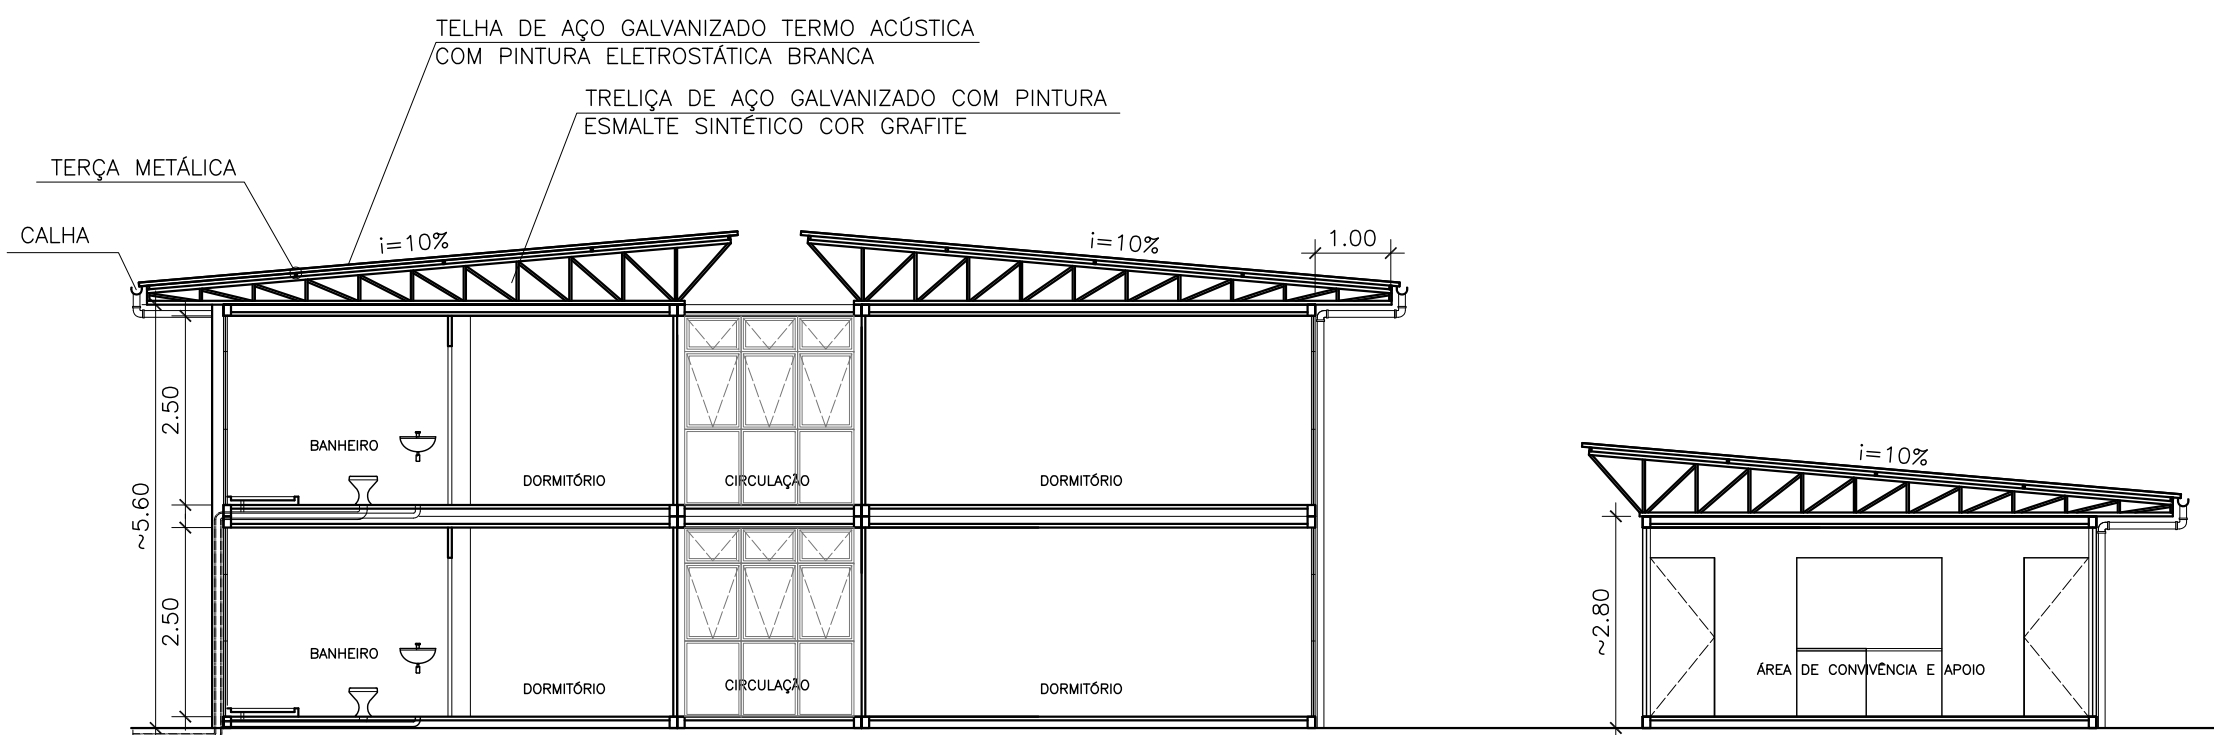


4 CORTE TRANSVERSAL AA
ESC.: 1:100

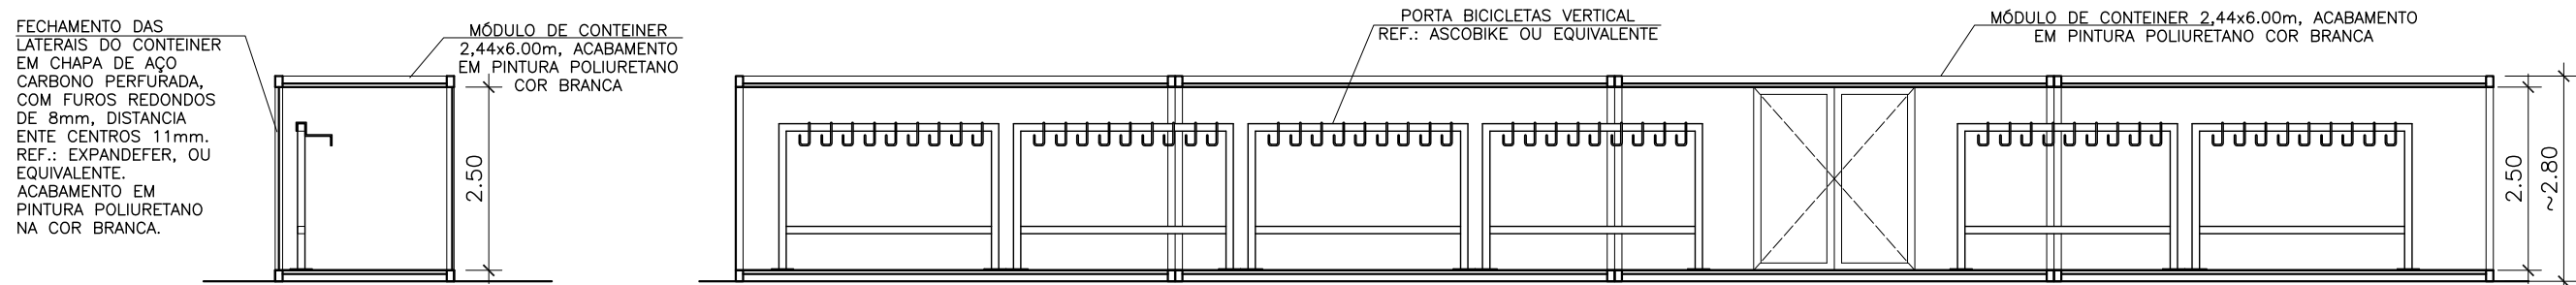


5 CORTE BB – BICICLETÁRIO
ESC.: 1:100

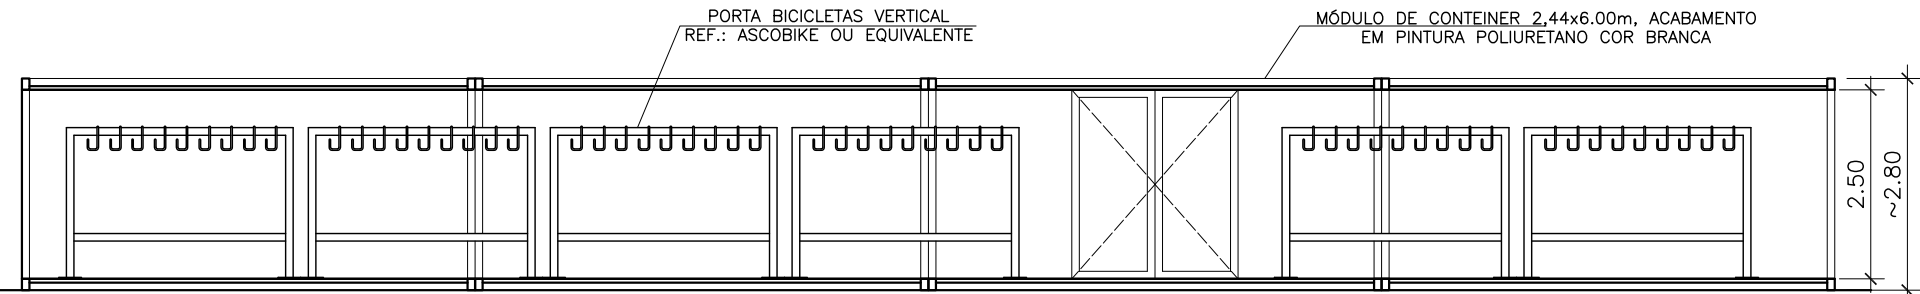

6 CORTE CC – BICICLETÁRIO
ESC.: 1:100

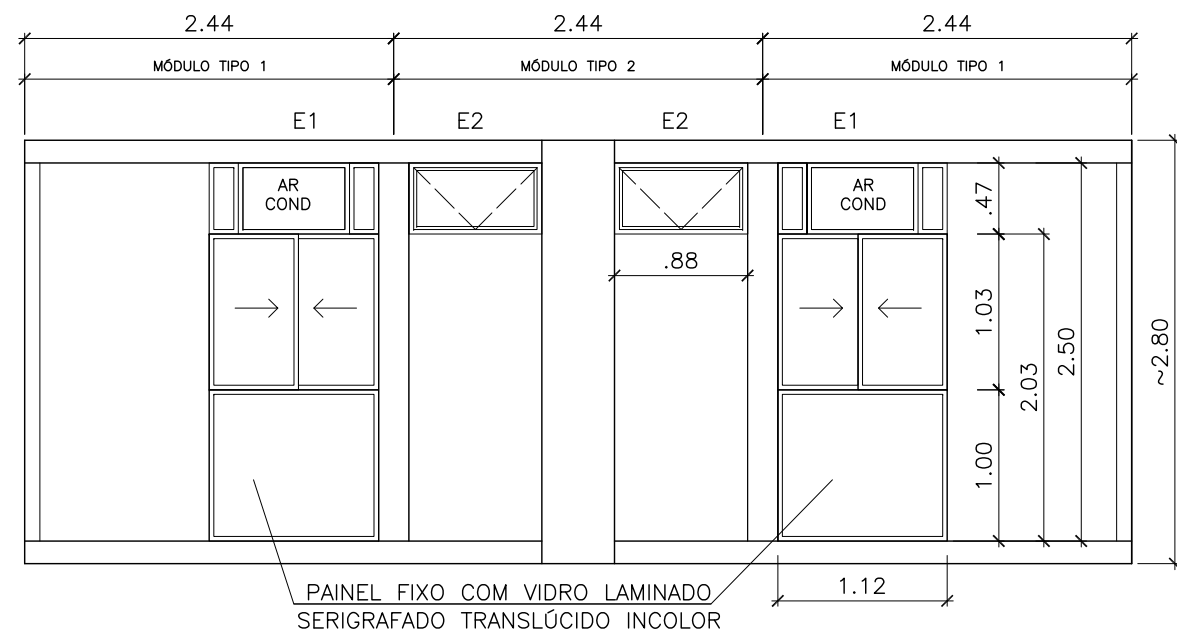

7 ELEVÇÃO TIPO DOS MÓDULOS DE ALOJAMENTO
ESC.: 1:50

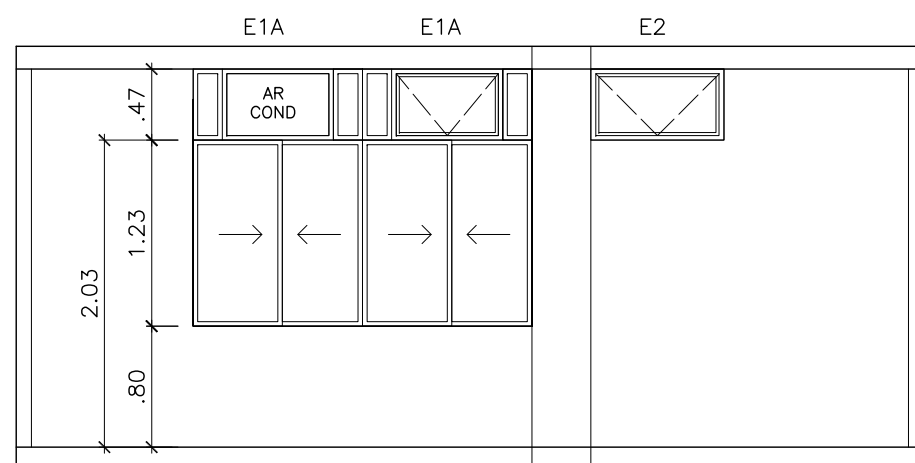

8 ELEVÇÃO TIPO MÓDULOS DE ALOJAMENTO PNE
ESC.: 1:50

ESPECIFICAÇÕES GERAIS DO CONTAINER:

MÓDULO: 6.00x2.44x2.50m

ESPECIFICAÇÕES DE MATERIAIS E ACABAMENTOS

PISOS

- 1 – PISO VINÍLICO EM MANTA, REF. TARKET, LINHA ABSOLUTE TISSÉ, 2mm 9233687, (TODOS OS QUARTOS, CIRCULAÇÕES E HALL).
- 2 – PISO EMBORRACHADO ANTIDERRAPANTE (BANHEIROS E ESCADAS).
- 3 – PISO B.O.V. ELEVADO COM VÁLVULA DE SAÍDA DE 1 1/2 POL. EM POLIÉSTER ALTO BRILHO REFORÇADO COM FIBRA DE VIDRO, COR BRANCA, REF.: ASTRA (DIMENSÕES 96x94x11cm), OU EQUIVALENTE. (EXCETO PARA BANHEIRO PNE).

PAREDES

- 1 – PINTURA COM TINTA POLIURETANO, NAS CORES:
 - 1A – AMARELO, REF.: PERFORTEK, AMARELO 001 412.
 - 1B – AZUL, REF.: PERFORTEK, AZUL MAR 508.
 - 1C – VERMELHO, REF.: PERFORTEK, VERMELHO SEGURANÇA 006.
 - 1D – VERDE, REF.: PERFORTEK, VERDE PETROBRAS.
 - 1E – BRANCO, REF.: PERFORTEK, BRANCO 001.

ORs: ESTAS TONALIDADES SERÃO DEFINIDAS COM AMOSTRAS ANTES DA EXECUÇÃO DA PINTURA.

TETO

- 1 – CHAPA DO MÓDULO PADRÃO PINTADA COM TINTA POLIURETANO NA COR BRANCA.

QUADRO DE ESQUADRIAS:

Nº	DIMENSÕES (cm)	DESCRIÇÃO	LOCAL	QUANT.
ESQUADRIAS				
E1	112 x 250	ESQUADRIA DE ALUMINIO COM PINTURA ELETROSTÁTICA COR BRANCO E VIDRO LAMINADO INCOLOR.	ALOJAMENTOS E ÁREA DE APOIO	88
E1A	112 x 250	ESQUADRIA DE ALUMINIO COM PINTURA ELETROSTÁTICA COR BRANCO E VIDRO LAMINADO INCOLOR.	ALOJAMENTOS PNE	04
E2	88 x 47	ESQUADRIA DE ALUMINIO COM PINTURA ELETROSTÁTICA COR BRANCO E VIDRO LAMINADO INCOLOR.	BANHEIROS E ÁREA DE APOIO	96
E3	244 x 250	ESQUADRIA DE ALUMINIO COM PINTURA ELETROSTÁTICA COR BRANCO E VIDRO LAMINADO INCOLOR.	CIRCULAÇÃO	12
E4	224 x 250	ESQUADRIA DE ALUMINIO COM PINTURA ELETROSTÁTICA COR BRANCO E VIDRO LAMINADO INCOLOR.	EXTREMOS DAS CIRCULAÇÕES	02
E5	244 x 250	ESQUADRIA DE ALUMINIO COM PINTURA ELETROSTÁTICA COR BRANCO E VIDRO LAMINADO INCOLOR.	ENTRADA	01

PORTAS

P1	80 x 210	DE ABRIR, EM PAINEL DE CHAPA METÁLICA COM TRATAMENTO ACÓSTICO, ACABAMENTO EM PINTURA POLIURETANO NA COR BRANCA.	ALOJAMENTOS E ÁREA DE APOIO	88
P2	60 x 210	DE ABRIR, EM PAINEL DE CHAPA METÁLICA COM TRATAMENTO ACÓSTICO, ACABAMENTO EM PINTURA POLIURETANO NA COR BRANCA.	BANHEIROS E ÁREA DE APOIO	80
P3	90 x 210	DE ABRIR, EM PAINEL DE CHAPA METÁLICA COM TRATAMENTO ACÓSTICO, ACABAMENTO EM PINTURA POLIURETANO NA COR BRANCA, CHAPA PARA PROTEÇÃO CONTRA CHOQUES, CONFORME NBR9050.	ALOJAMENTOS PNE E BANHEIROS DA ÁREA DE APOIO	04
P4	224 x 210	DE ABRIR, 02 FOLHAS, QUADRO MONTANTE EM PERFIL TUBULAR QUADRADO DE AÇO GALVANIZADO COM PINTURA POLIURETANO COR BRANCA E VIDRO LAMINADO INCOLOR.	ENTRADA	01
PA4	200 x 210	DE ABRIR, 02 FOLHAS, QUADRO MONTANTE EM PERFIL TUBULAR QUADRADO DE AÇO GALVANIZADO COM PINTURA POLIURETANO COR BRANCA E VIDRO LAMINADO INCOLOR.	ENTRADA ÁREA DE APOIO	01
P5	200 x 250	DE ABRIR, 02 FOLHAS, QUADRO MONTANTE EM PERFIL TUBULAR DE AÇO GALVANIZADO E CHAPA DE AÇO CARBONO PERFORADA COM Furos Redondos de 8mm, DISTÂNCIA ENTRE CENTROS 11mm, REF.: EXPANDEFER, OU EQUIVALENTE, ACABAMENTO EM PINTURA POLIURETANO NA COR BRANCA.	BICICLETÁRIO	01
P6	200 x 210	DE ABRIR, EM PAINEL DE CHAPA METÁLICA COM TRATAMENTO ACÓSTICO, ACABAMENTO EM PINTURA POLIURETANO NA COR BRANCA.	DEPÓSITO	01

01	EMISSÃO INICIAL	23/10/15	SG	
REV.	DESCRIÇÃO	DATA:	DES.:	APROV.:

- NOTAS:
1. ÁREAS APROXIMADAS.
 2. DUAS OPÇÕES DE LAYOUT A CRITÉRIO DO USUÁRIO.
 3. 80 SUITES DUPLAS, SENDO 2 PARA PESSOAS PNE. CAPACIDADE= 164 PESSOAS.

UNIVERSIDADE FEDERAL DO RIO DE JANEIRO			
ESCRITÓRIO TÉCNICO DA UNIVERSIDADE - ETU			
COORDENAÇÃO DE PROJETOS			
TÍTULO		PROJETO	
ALOJAMENTO / CCMN		ARQUITETURA	
ALOJAMENTO MODULAR DE CONTAINER			
LOCAL		FASE	
CIDADE UNIVERSITÁRIA - ILHA DO FUNDÃO		ESTUDO PRELIMINAR	
CONTEÚDO		CÓD.	
FACHADAS E CORTES		2015.006	
DIRETOR DO ETU		ARQUIVO	
		2015.006.ALQJ_CONT-04-CRT-FAC-ARQ-ESP-00	
AUTOR(ES) DO PROJETO		ESC.	
		DIVERSA	
COORD. PROJ.: ALEXANDRE A. S. MARTINS		DATA	
ARQUITETO - CREA - RJ 54.442 D		OUTUBRO/2015	
MIGUEL FONTES PINHEIRO		DES.	
ARQUITETO - CREA - RJ 42.385 D		PRANCHA	
MÁRIO ESCOBAR CONFORTE		4/4	
ENG. MECÂNICO - SBAPE 0364862			