



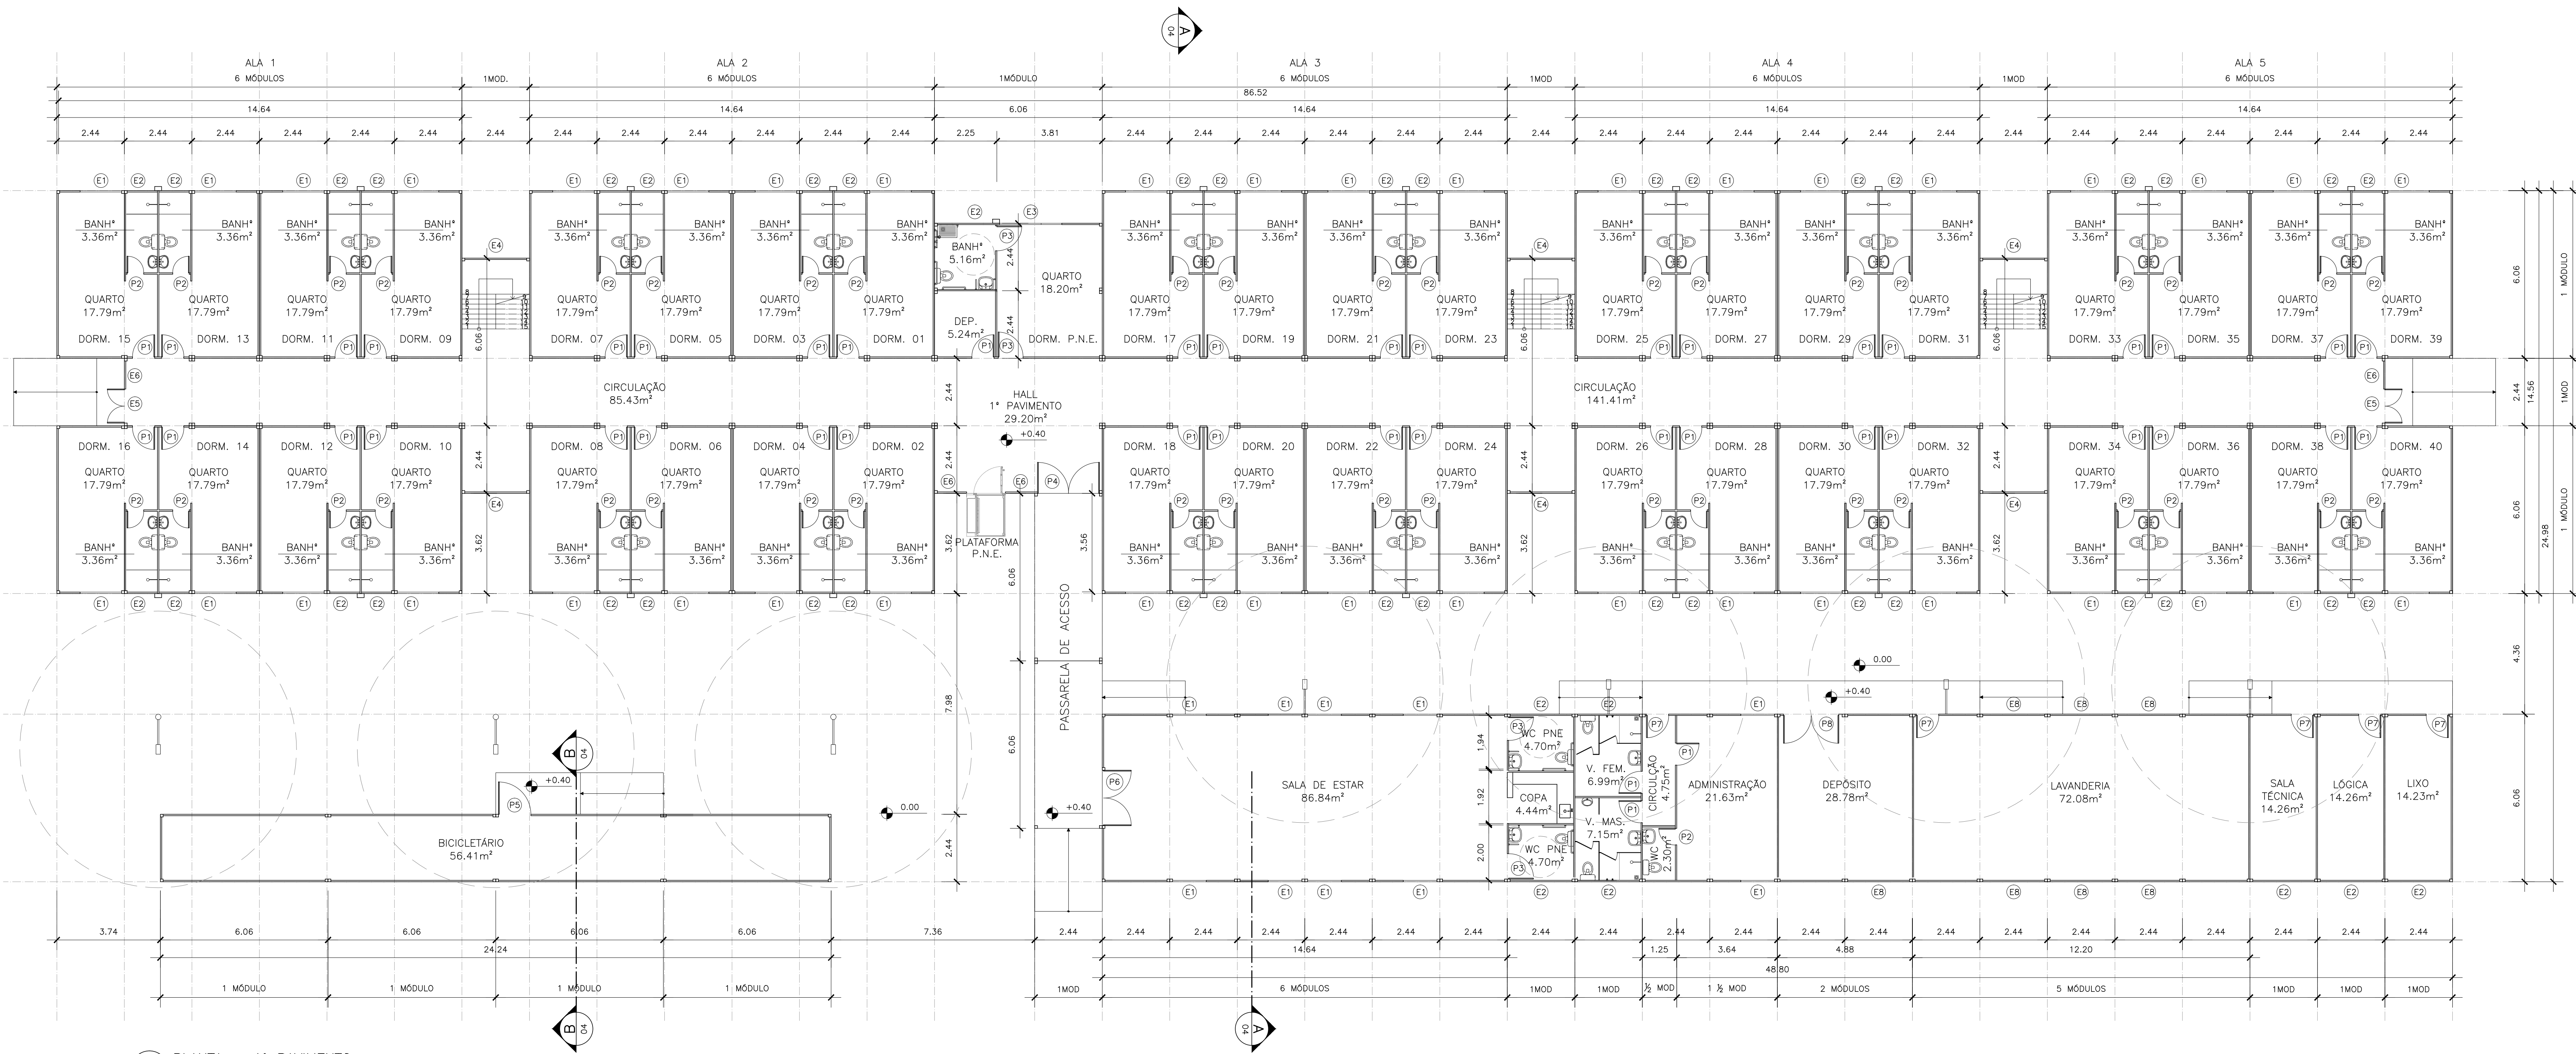

1 PLANTA — 1.º PAVIMENTO
ESC.: 1:100

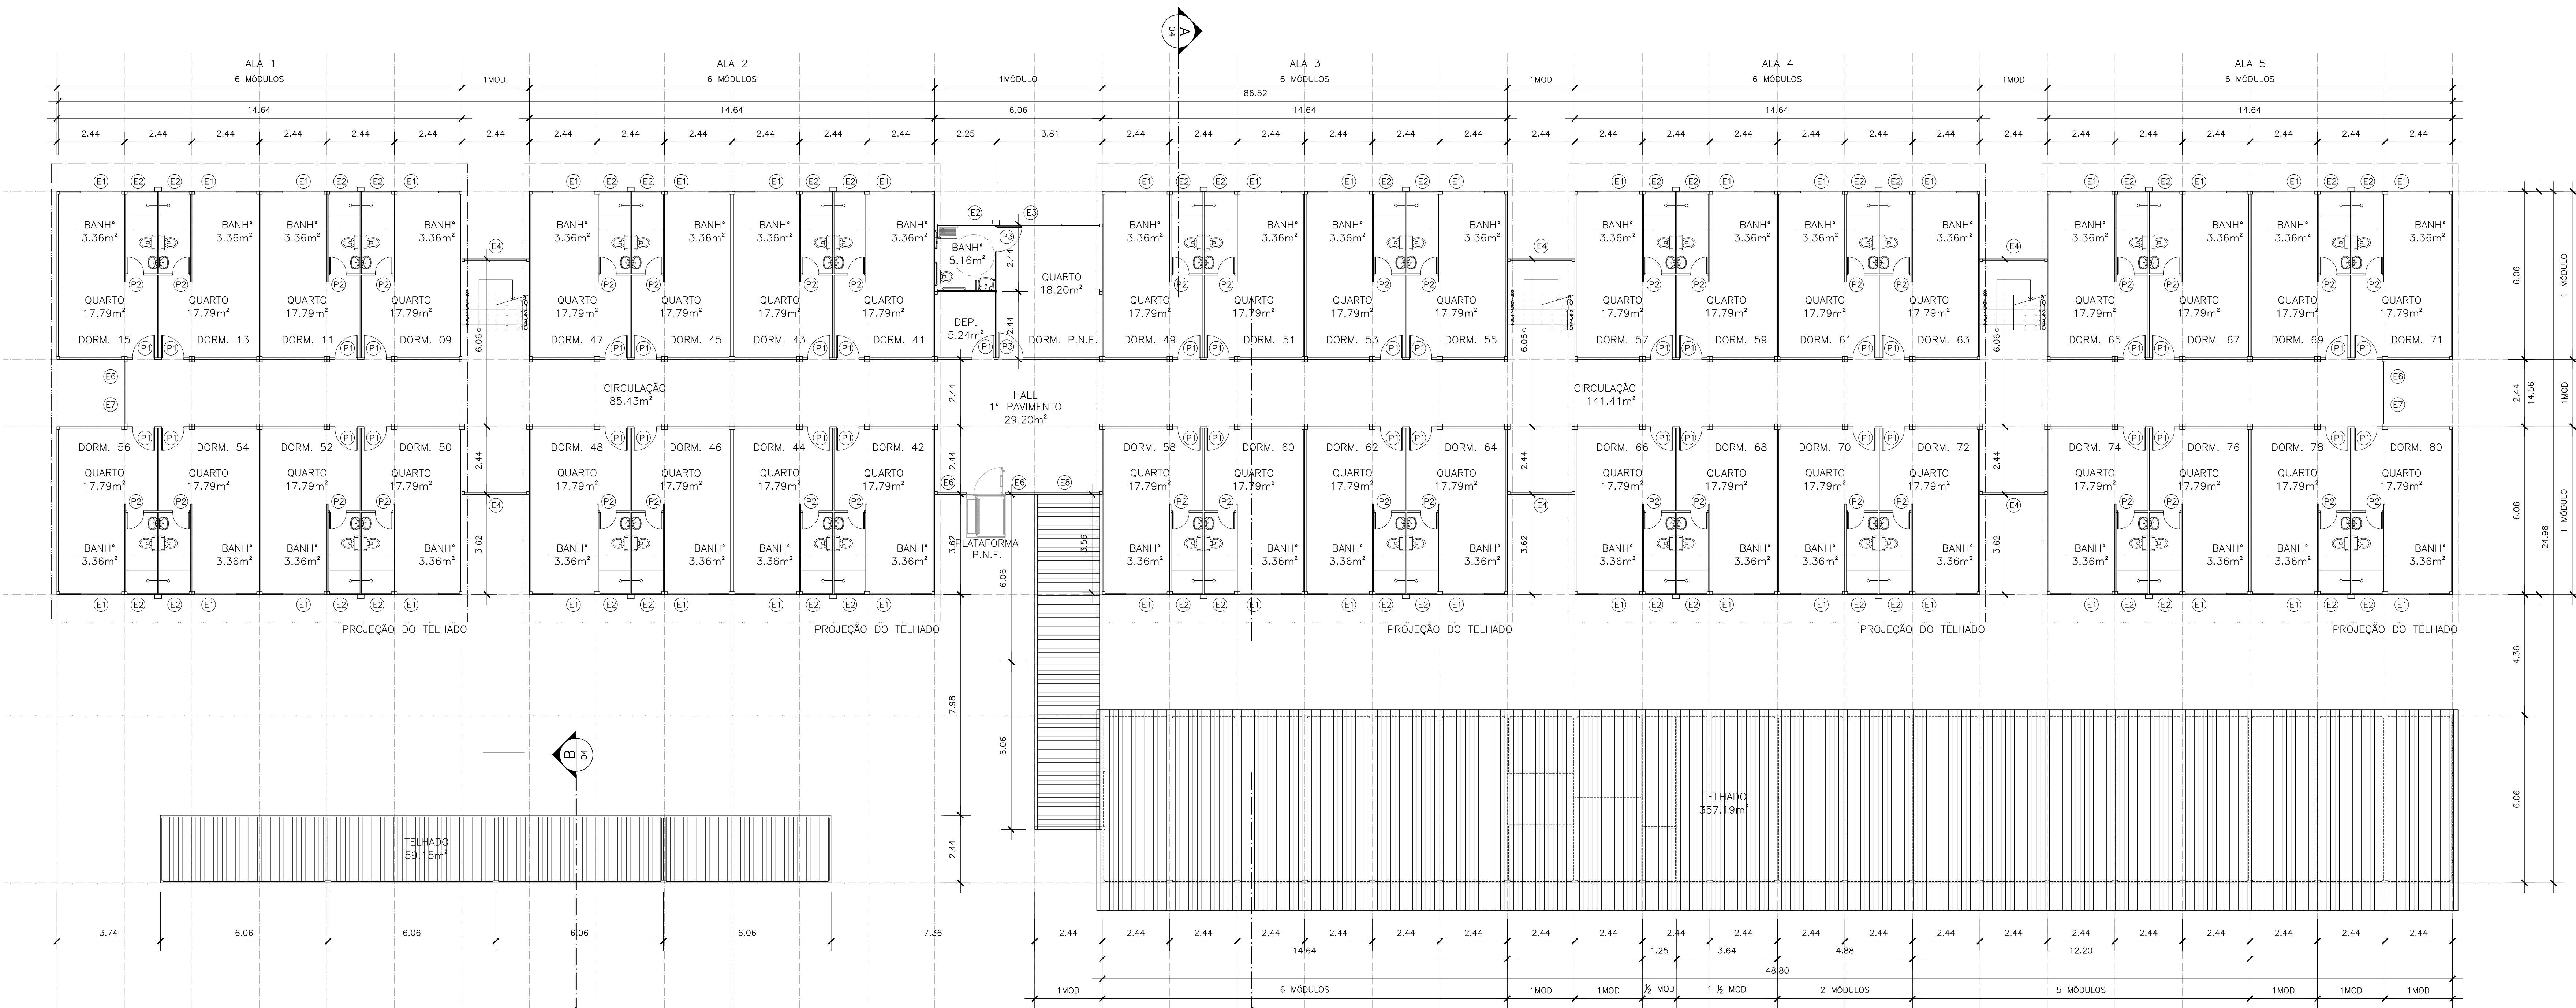

2 PLANTA — 2.º PAVIMENTO
ESC.: 1:100

NOTAS GERAIS			
REF.	DESCRIÇÃO		
01.	Todas as cotas estão em metros, salvo quando indicadas no desenho.		
02.	Os módulos não devem ser colocados diretamente no solo. Devem ser apoiados em blocos de concreto armado.		
03.	Piso sob os módulos deverá ser regularizado de forma a evitar a penetração e o acúmulo de água sob os mesmos.		
QUADRO DE ÁREAS			
DESCRIÇÃO		ÁREA ÚTIL	ÁREA CONSTRUÍDA
PRIMEIRO PAVIMENTO		1132,81m²	1177,42m²
SEGUNDO PAVIMENTO		1132,81m²	1177,42m²
TELHADO (ALCANTARAL)		100,90 m²	-
PASSARELA		29,55m²	29,55m²
ANEXO		343,52m²	354,87m²
TELHADO (ANEXO)		357,19 m²	-
SUBSTACIAÇÃO		54,39m²	55,00m²
TOTAL		-	2799,26 m²

QUADRO DE ESQUADRIAS											
1. PORTAS											
REF.	VÃO ACABADO	1PAV	2PAV	ANX	SBST	REF.	VÃO ACABADO	1PAV	2PAV	ANX	SBST
P1	0,80m x 2,10m	41	41	3	-	P6	2,00m x 2,10m	-	-	1	-
P2	0,60m x 2,10m	40	40	2	-	P7	0,80m x 2,50m	-	-	5	-
P3	0,90m x 2,10m	2	2	2	-	P8	2,00m x 2,50m	-	-	1	-
P4	2,24m x 2,10m	1	-	-	-	P9	1,60m x 2,50m	-	-	-	2
P5	2,11m x 2,10m	-	-	1	-	-	-	-	-	-	-

2. JANELAS											
REF.	VÃO ACABADO	1PAV	2PAV	ANX	SBST	REF.	VÃO ACABADO	1PAV	2PAV	ANX	SBST
E1	1,50m x 2,50m	40	40	-	-	E6	1,01m x 2,50m	4	4	-	-
E2	0,95m x 0,50m	41	41	8	-	E7	1,23m x 2,50m	-	2	-	-
E3	2,25m x 2,50m	1	1	-	-	E8	2,00m x 2,50m	-	-	7	-
E4	2,24m x 2,50m	6	7	-	-	-	-	-	-	-	-
E5	1,23m x 2,50m	2	-	-	-	-	-	-	-	-	-

PISO	
REF.	DESCRIÇÃO
1	Panel Wall: Placa de madeira laminada ou serrada, construída em ambas as faces por lâminas de madeira, e externamente por placas cerâmicas CRFS (Cimento Reforçado com Fibras Sintéticas) prensadas, e = 23mm, com capacidade de carga de 300kg/m². REF. BRASIL: Madeirland 20mm, ou equivalente.
2	Piso vinílico em manta, e = 2mm. REF. TARKET, Linha Absolute Test, cod. 9233687, ou equivalente.
3	Piso emborrachado antiderrapante.
4	PIPO BOX elevado com válvula de saída de 1 1/2", em políester alto brilho reforçado com fibra de vidro, cor branca. REF. ASTRA, 0,90m x 0,90m x 0,12m, ou equivalente.
5	PIPO BOX elevado com o piso do banheiro, com válvula de saída de 1 1/2", em políester alto brilho reforçado com fibra de vidro, cor branca. REF. ASTRA, 0,90m x 0,90m x 0,12m, ou equivalente.

ALA 1	Painéis Fachada: Face Interna: Cor branca, REF.: PERFORTEK, Branco 001. Face Externa: Cor amarelo, REF.: PERFORTEK, Amarelo 1021 412. Painéis Internos: Face Interna: Cor branca, REF.: PERFORTEK, Branco 001. Face Externa: Cor branca, REF.: PERFORTEK, Branco 001.
ALA 2	Painéis Fachada: Face Interna: Cor branca, REF.: PERFORTEK, Branco 001. Face Externa: Cor azul, REF.: PERFORTEK, Azul 558. Painéis Internos: Face Interna: Cor branca, REF.: PERFORTEK, Branco 001. Face Externa: Cor branca, REF.: PERFORTEK, Branco 001.
ALA 3	Painéis Fachada: Face Interna: Cor branca, REF.: PERFORTEK, Branco 001. Face Externa: Cor vermelho, REF.: PERFORTEK, Vermelho Segurança 00. Painéis Internos: Face Interna: Cor branca, REF.: PERFORTEK, Branco 001. Face Externa: Cor branca, REF.: PERFORTEK, Branco 001.
ALA 4	Painéis Fachada: Face Interna: Cor branca, REF.: PERFORTEK, Branco 001. Face Externa: Cor verde, REF.: PERFORTEK, Verde Perolado. Painéis Internos: Face Interna: Cor branca, REF.: PERFORTEK, Branco 001. Face Externa: Cor branca, REF.: PERFORTEK, Branco 001.
ALA 5	Painéis Fachada: Face Interna: Cor branca, REF.: PERFORTEK, Branco 001. Face Externa: Cor verde, REF.: PERFORTEK, Verde Perolado. Painéis Internos: Face Interna: Cor branca, REF.: PERFORTEK, Branco 001. Face Externa: Cor branca, REF.: PERFORTEK, Branco 001.

ANELA	Painéis Fachada: Face Interna: Cor branca, REF.: PERFORTEK, Branco 001. Face Externa: Cor branca, REF.: PERFORTEK, Branco 001. Painéis Internos: Face Interna: Cor branca, REF.: PERFORTEK, Branco 001. Face Externa: Cor branca, REF.: PERFORTEK, Branco 001.
-------	---

2	CHAPA DE AÇO: Chapa de aço carbono perfurada, com furo de 10mm, distância entre-eixos de 14mm, dispostos de forma alternada longitudinal, na cor natural. REF.: PERMETAL, ou equivalente.
---	---

3	CHAPA DE AÇO: Chapa de aço carbono perfurada, com furo de 8mm, distância entre-eixos de 10mm, dispostos de forma alternada longitudinal, na cor natural. REF.: PERMETAL, ou equivalente.
---	--

REF.	DESCRIÇÃO										
1	Painel termocíclico composto por três camadas dispostas da seguinte forma: na face externa, telha trapezoidal com espessura e = 1,00mm; na face interna, lâmina de espessura de 0,50mm com pintura em tinta à base de poliuretano (PU). Na camada interior, espuma de poliuretano, com coeficiente de isolamento térmico (R) igual a 0,020 W/m².K, com espessura mínima e = 40mm, ou material equivalente com capacidade de isolamento térmico igual ou superior.										

REF.	DESCRIÇÃO	1PAV	2PAV	ANX	SBST
1	Bacia sanitária com caixa acoplada, com acionamento dual, cor branco gelo. REF.: DECA, Linha Vogue Plus, modelo P.505.37 e CD.01F.37, ou equivalente.	40	40	3	-
2	Bacia sanitária convencional conforto, sem abertura frontal. REF.: DECA, Linha Vogue Plus, modelo P.501.17 ou equivalente.	1	1	2	-
3	Lavatório com coluna, cor branco gelo. REF.: DECA, Linha Vogue Plus, modelo L.51.17 e C.1.17 ou equivalente.	40	40	3	-
4	Lavatório com coluna suspensa, cor branco gelo. REF.: DECA, Linha Vogue Plus, modelo L.51.17 e C.1.17 ou equivalente.	1	1	2	-
5	Torneira de mesa com fechamento automático para lavatório, cor cromado. REF.: DECA, Linha DECAMATIC ECO, modelo 1173.C.CONF. ou equivalente.	1	1	2	-
6	Torneira de mesa para lavatório, cor cromado. REF.: DECA, Linha ASPEN, modelo 1198.C35 ou equivalente.	40	40	3	-
7	Módulo com apoio integrado, cor branco gelo. REF.: DECA, modelo M715 ou equivalente.	-	-	1	-
8	Chuveiro de Chuveiro 550W 12V 3 Temp, cor branco. REF.: LORENZETTI, Bello Bello, ou equivalente.	41	41	4	-
9	Barra de apoio 80cm, aço inox. REF.: DOCOL, código 0044616 ou equivalente.	2	2	4	-
10	Barra de apoio 80cm, aço inox. REF.: DOCOL, código 0044616 ou equivalente.	1	1	-	-
11	Barra de apoio 35cm, aço inox. REF.: DOCOL, código 2528025 ou equivalente.	2	2	4	-
12	Barra de apoio 35cm, aço inox. REF.: DOCOL, código 2528025 ou equivalente.	1	1	-	-
13	Barra de apoio 80cm, aço inox. REF.: DOCOL, código 0044616 ou equivalente.	1	1	-	-
14	Barra de apoio 35cm, aço inox. REF.: DOCOL, código 2528025 ou equivalente.	2	2	4	-
15	Porta papel sanitário, em alumínio maciço, com acabamento cromado.	41	41	5	-
16	REF.: MODELNIX, Linha Angola, cod. 0148, ou equivalente.	82	82	-	-
17	Toalheiro para Papel Toalha. REF.: COLUMBUS, Dispenser Fumê, cod. 99.1012, ou equivalente.	-	-	5	-
18	Plataforma de vidro, com suporte em alumínio maciço, com acabamento cromado.	41	41	2	-

REF.	DESCRIÇÃO										
1	Plataforma elevatória para acessibilidade. Dimensão 1,40m x 1,50m. Estrutura em aço inox, com acabamento em alumínio pigmentado (ACM), cor grafite. REF.: MONTELE, Mod. PL240 ou equivalente.										
01	EMISSÃO: INICIAL										
REV.	DESCRIÇÃO										

UNIVERSIDADE FEDERAL DO RIO DE JANEIRO										
ESCRITÓRIO TÉCNICO DA UNIVERSIDADE - ETU										
COORDENAÇÃO DE PROJETOS										
TÍTULO					ALOJAMENTO / CCNM					PROJETO
LOCAL					ALOJAMENTO ESTUDANTIL EM MÓDULOS METÁLICOS HABITÁVEIS					ARQUITETURA
CONTÉUDO					PLANTAS					FASE
RUA MILTON SANTOS, Nº 75 - CIDADE UNIVERSITÁRIA - ILHA DO FUNDAÇÃO - RJ										COD.
										ANEXAMENTO
										PROJ. Nº 001.000.0